

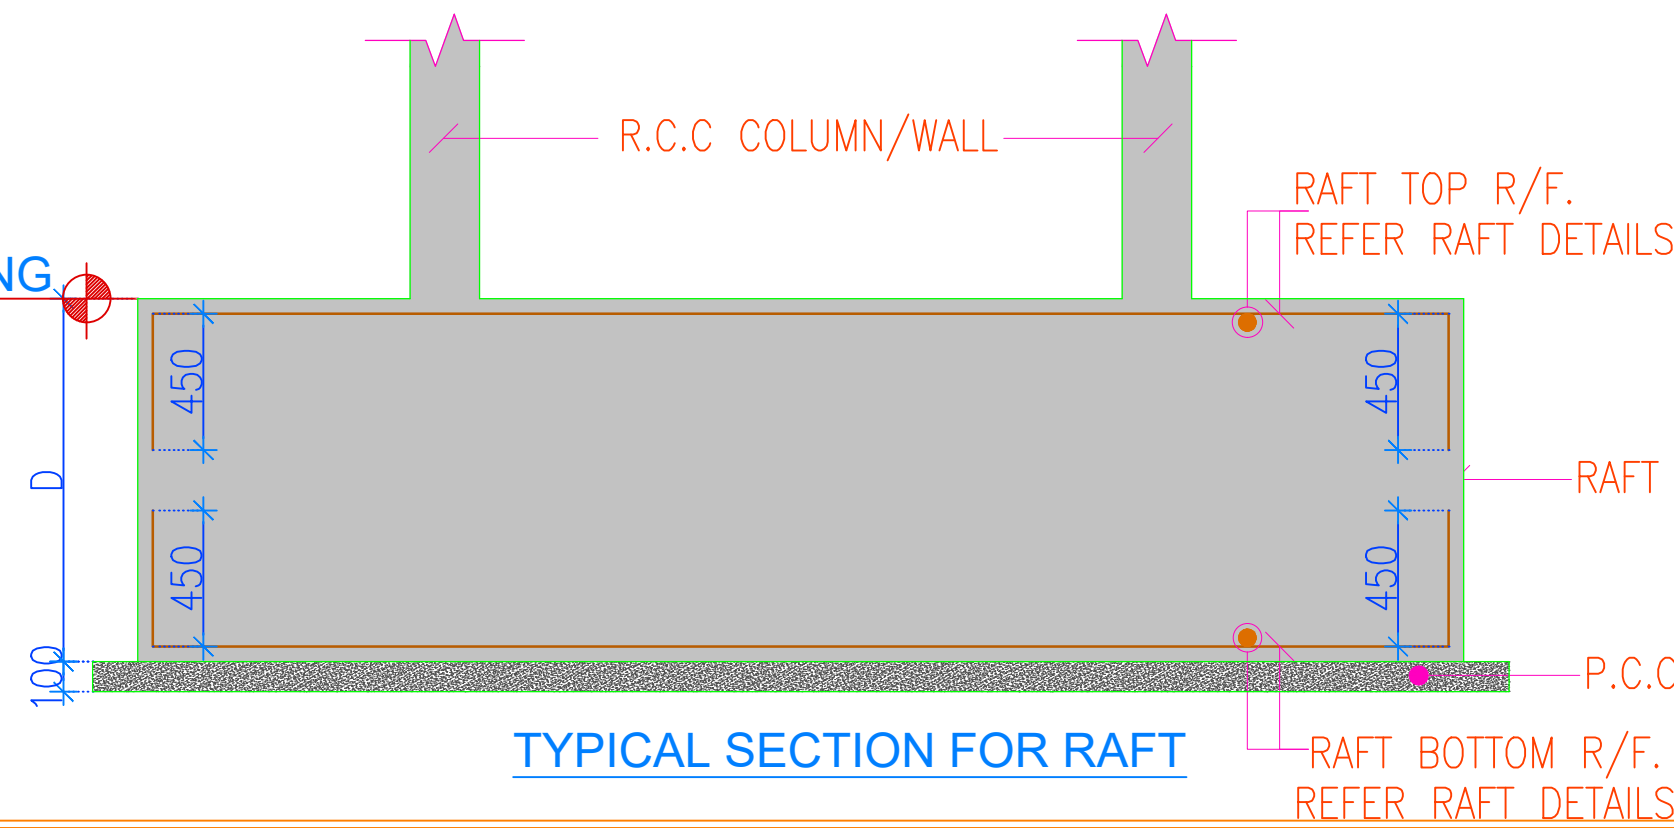
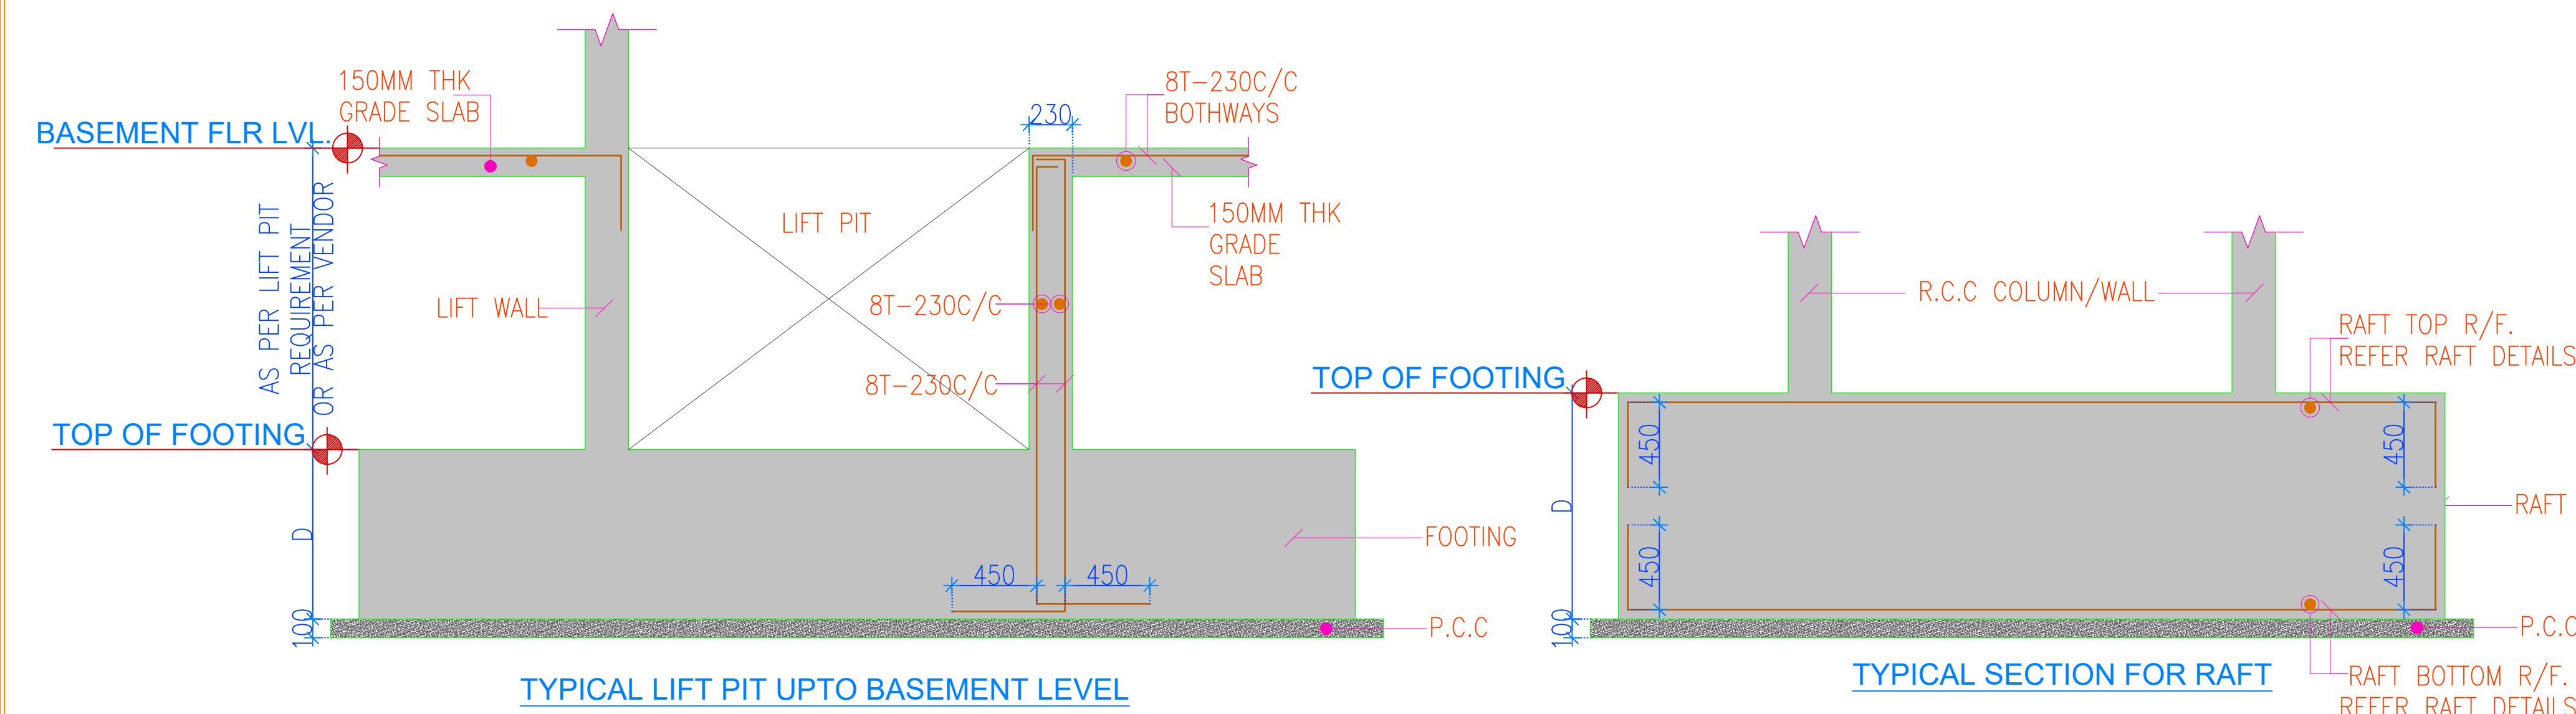
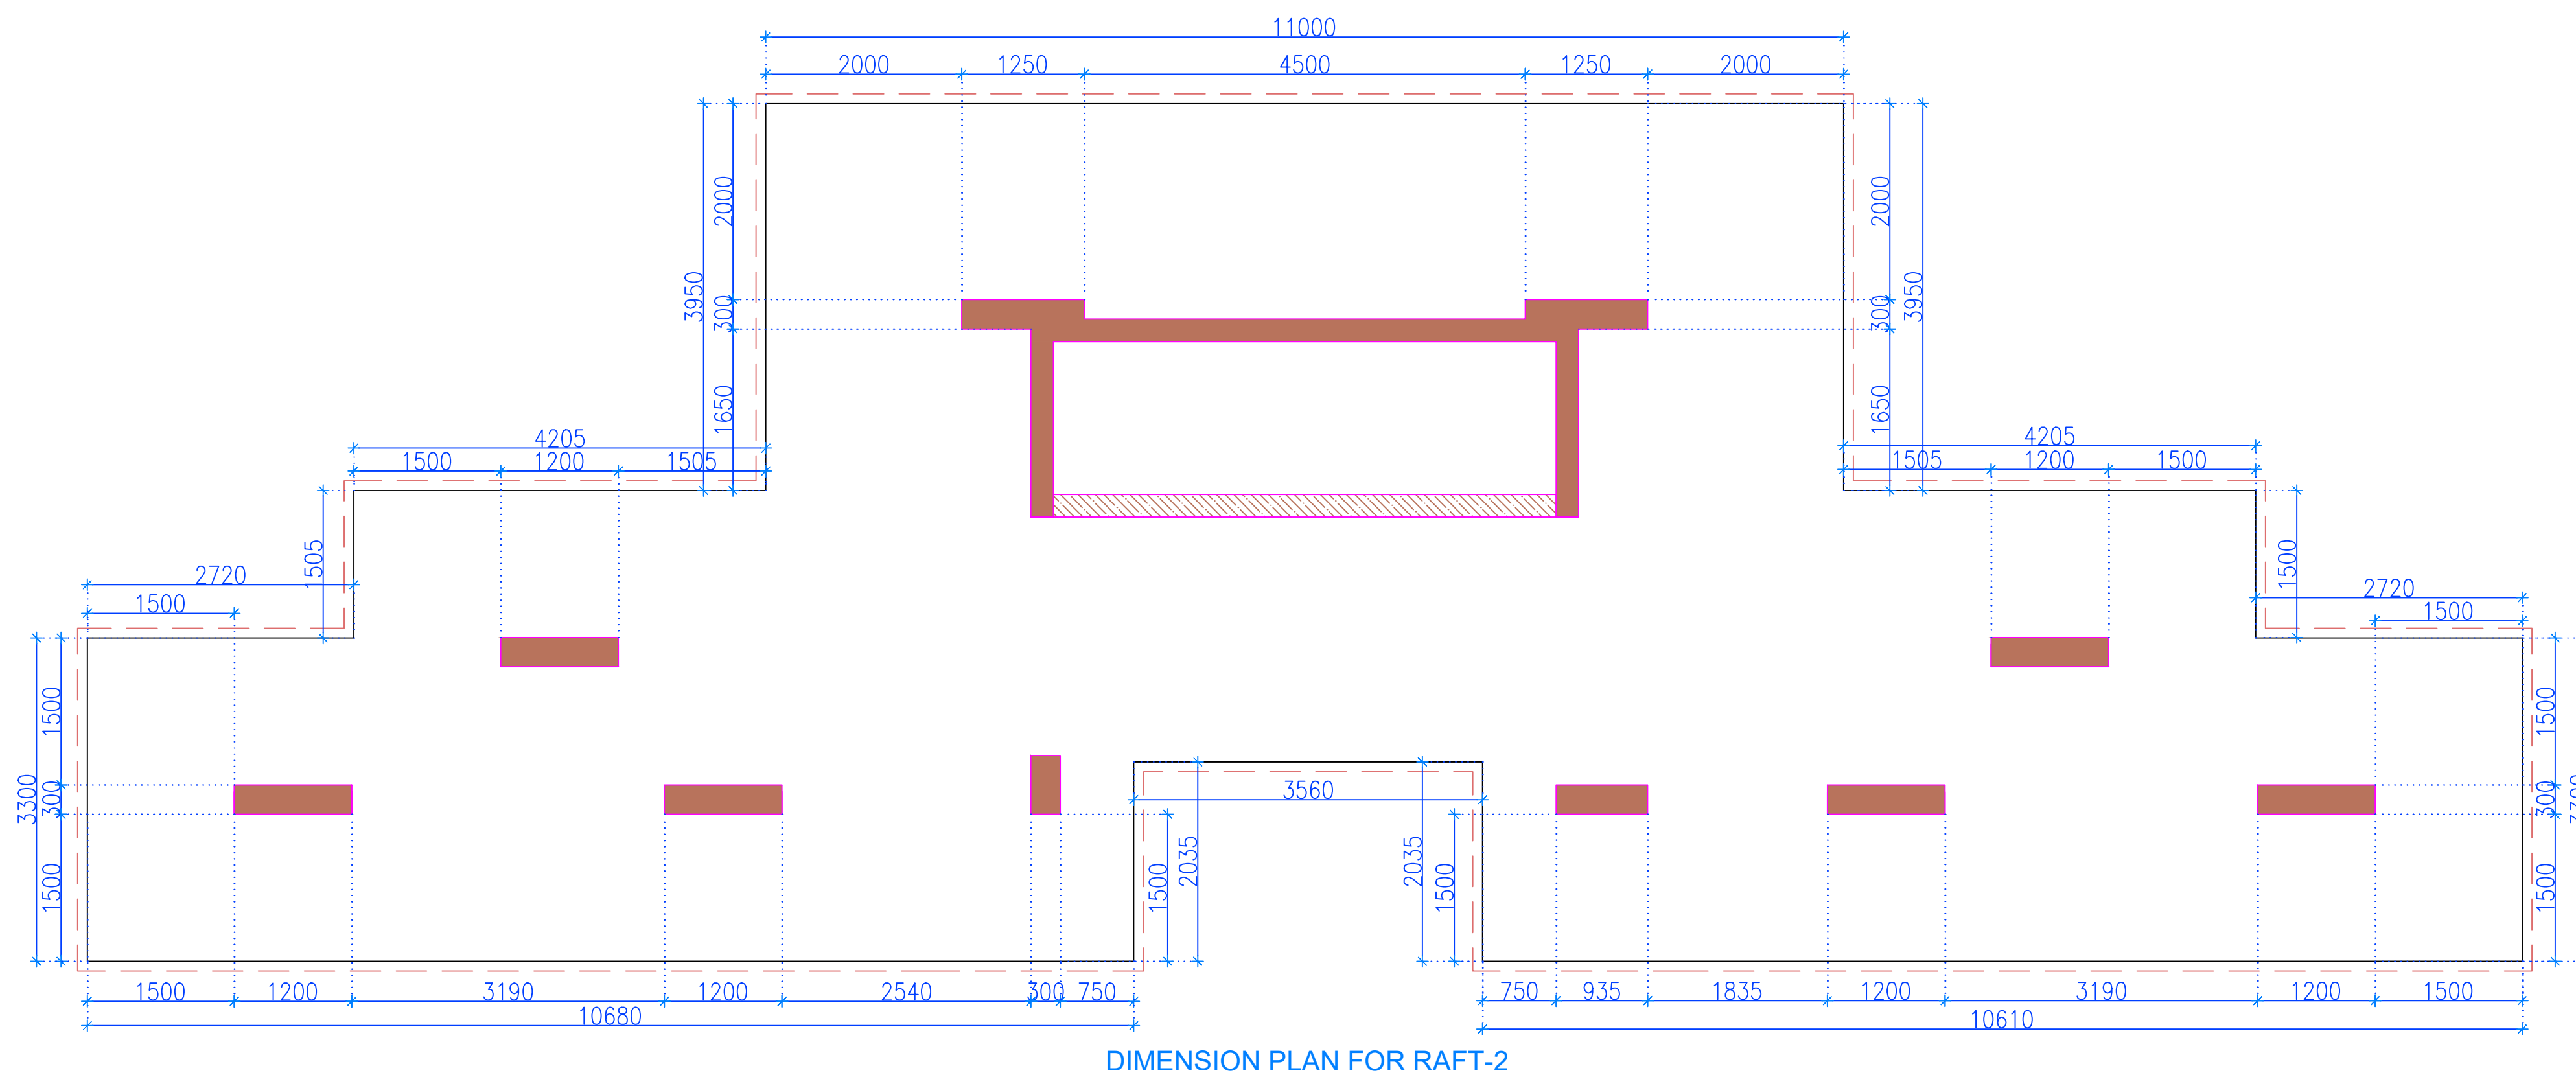
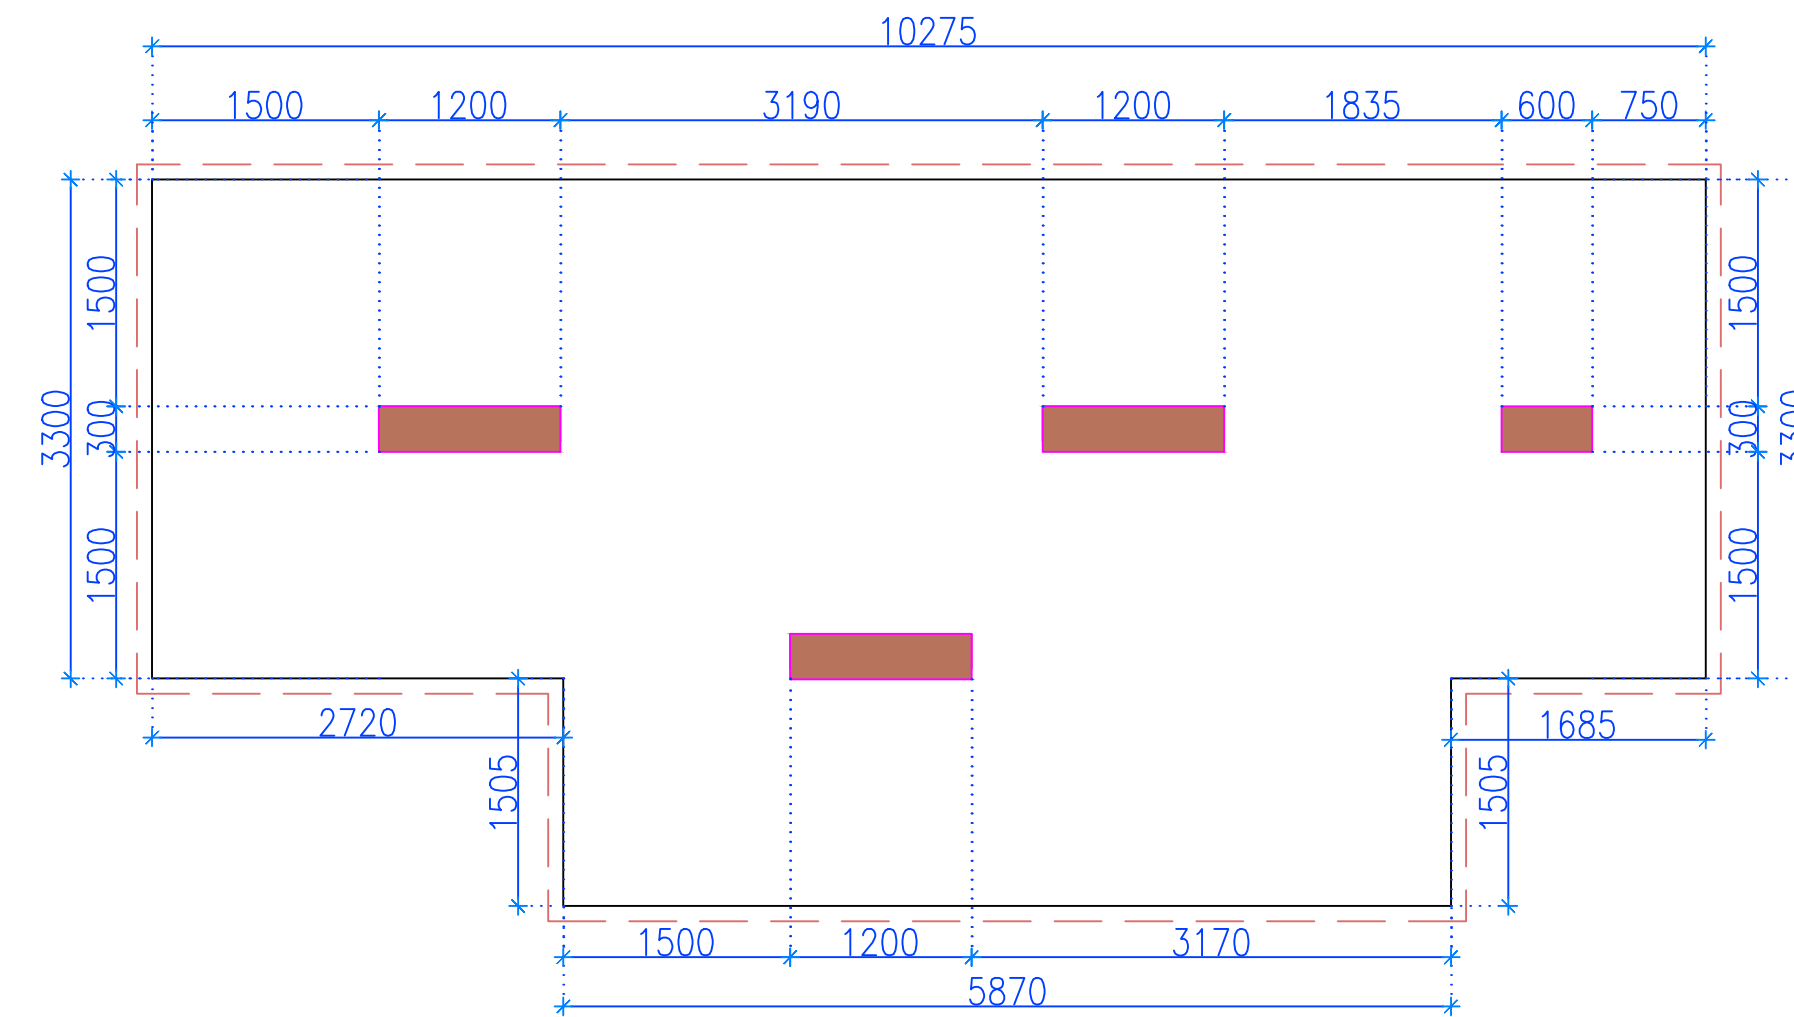


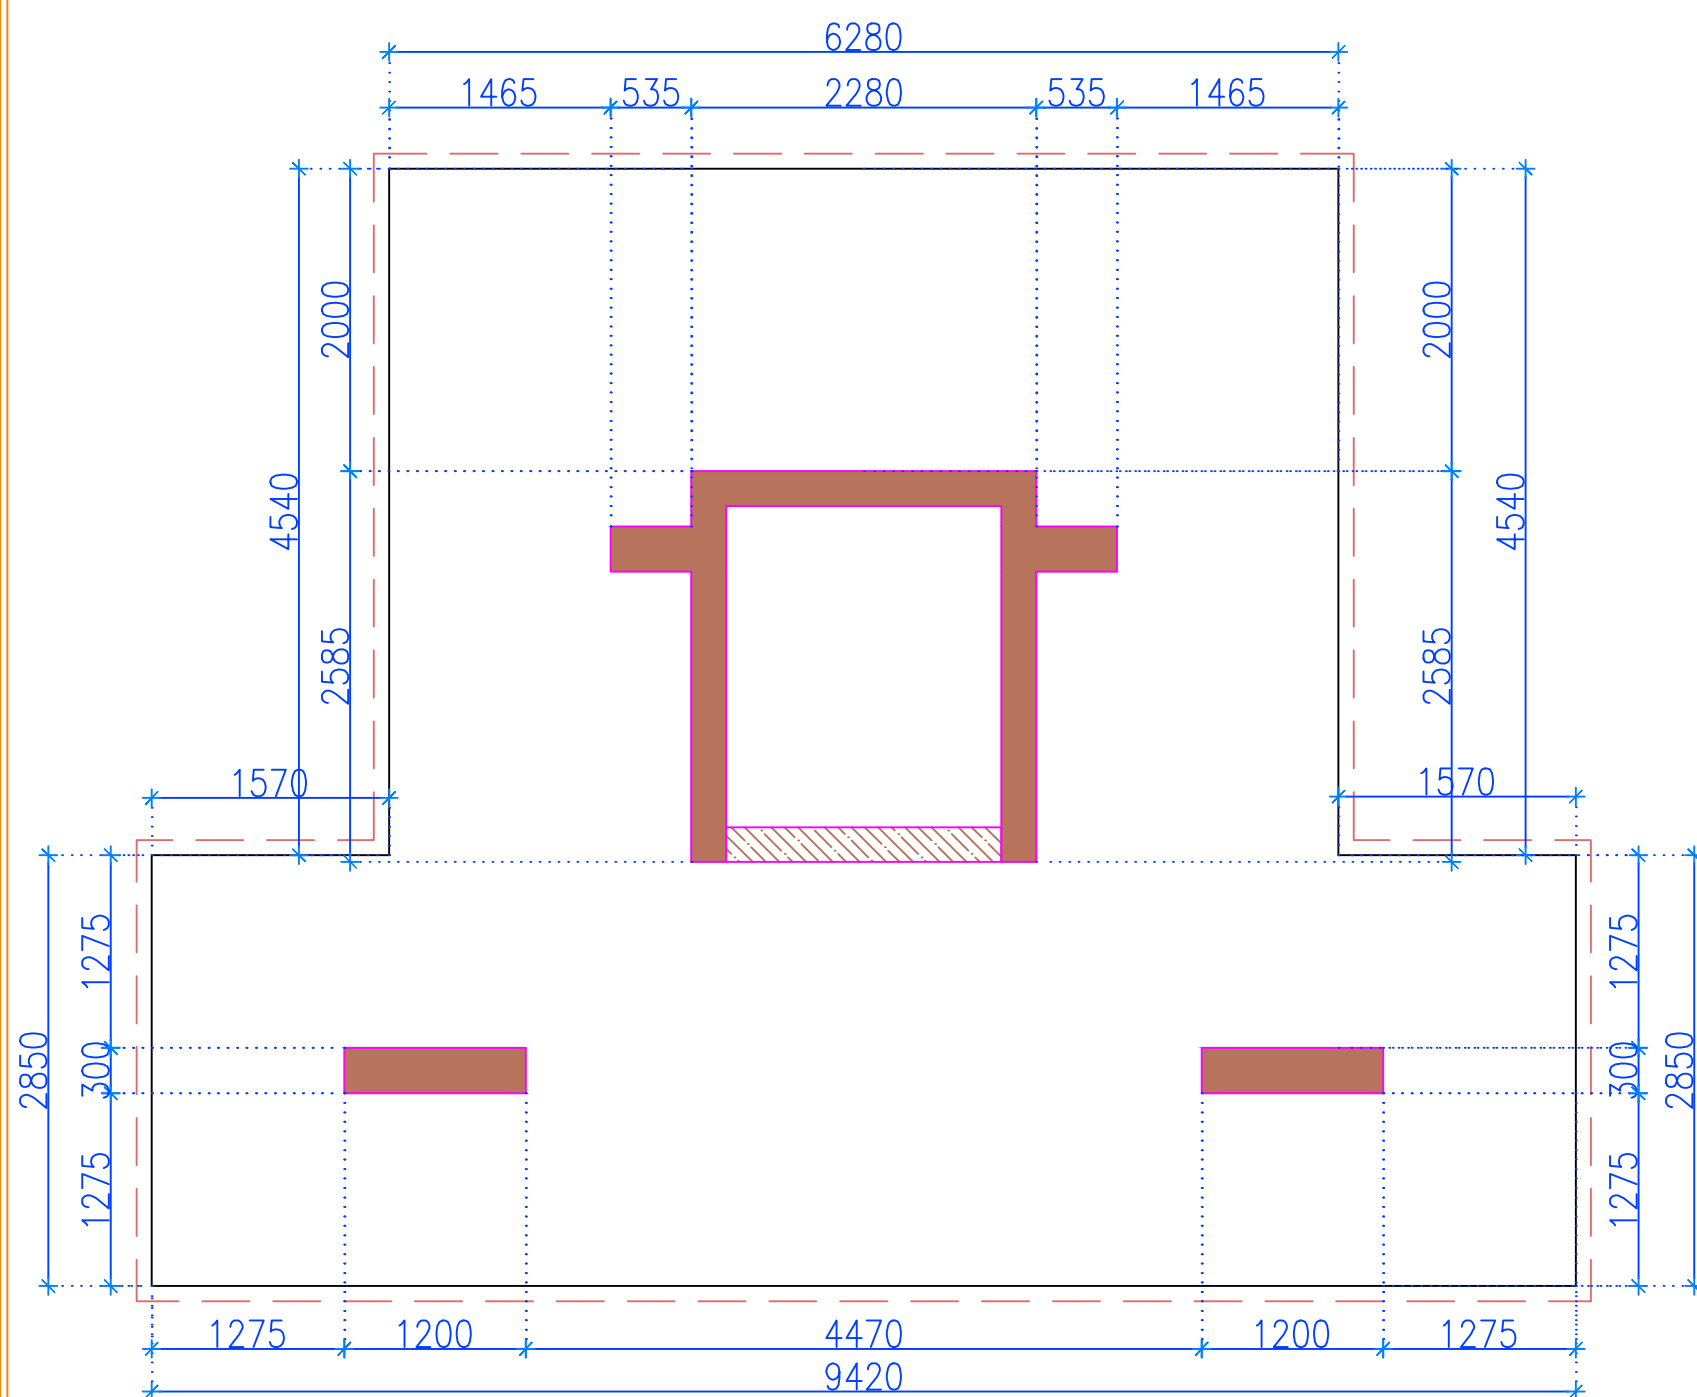

FOOTING SCHEDULE			
	RAFT-1	RAFT-2	RAFT-3
B' x L' (PCC)	REFER PLAN	REFER PLAN	REFER PLAN
B x L			
D	1000	1000	1000
T	—	—	—
STEEL // - B (SHORT SIDE) (BOTTOM FACE)	16T-100C/C	16T-100C/C	16T-100C/C
STEEL // - L (LONG SIDE) (BOTTOM FACE)	16T-100C/C	16T-100C/C	16T-100C/C
STEEL // - B (SHORT SIDE) (TOP FACE)	16T-100C/C	16T-100C/C	16T-100C/C
STEEL // - L (LONG SIDE) (TOP FACE)	16T-100C/C	16T-100C/C	16T-100C/C
REMARK	PAD FOOTING	PAD FOOTING	PAD FOOTING

- ### GENERAL NOTES :-
1. ALL DIMENSIONS ARE IN MM.
 2. FOR ALL NOTES, REFER OUR DRG NO: S0-01 TO S0-09.
 3. CEMENT SHALL BE OPC 43 GRADE OR HIGHER / AS PER TENDER SPECIFICATIONS & PORTABLE WATER SHOULD BE USE.
 4. SUPERVISION SHALL NOT BE OUR RESPONSIBILITY.
 5. TO TAKE OUT THE CUBE AND MATERIAL TESTING SHALL BE CONTRACTOR/ BUILDER/CLIENTS RESPONSIBILITY.
 6. LOAD TESTING OF STRUCTURE SHALL NOT BE OUR RESPONSIBILITY.
 7. ALL DIMENSIONS ARE TO BE READ AND NOT TO BE MEASURED
 8. T OR # INDICATE STEEL FE 5000 GRADE TMT BARS.
 9. ALL CONC.MIX. M:30 UNLESS OTHERWISE SPECIFIED.
 10. LD = DEVELOPMENT LENGTH : $50 \times \phi$; WHERE, ϕ = DIA. OF BAR.
 11. ALL BRICK WORK SHALL BE IN C.M. (1:6)
 12. STRUCTURAL LAY OUT SHOULD BE REFER ONLY FOR STRUCTURAL DETAILING.
 13. PLEASE REFER ARCHITECTURAL DWG FOR LVLS. & SETTINGS OUT CENTERLINE DIMENSIONS. THE CENTERLINE PUT IN THIS STRUCTURAL FOUNDATION LAYOUT IS SIMPLY INDICATIVE OF LOCATION AND AS APPROVED BY ARCHITECT.
 14. PLEASE REFER ARCH. DWG. FOR FINAL LAY OUT.
 15. CONTRACTOR SHOULD INFORM ARCHITECT/STRUCTURAL CONSULTANT IN CASE OF ANY CHANGE IN EXISTING CONDITION FOUND, IMMEDIATELY
 16. THIS DRG. SHOULD BE READ ALONG WITH ARCHITECTURAL DRGS. AND ANY CHANGES/DEVIATION FOUND SHOULD BE IMMEDIATELY BROUGHT TO NOTICE OF ARCHITECT & STR. ENGINEER
 17. THIS DWG.SHOULD BE READ ALONG WITH RELEVANT DETAILS
 18. MIX DESIGN SHOULD BE GOT APPROVED PRIOR TO EXECUTION OF WORK
 19. ALL STEEL (TOP/BOTTOM) OF DIFFERENT TYPE SHALL BE LAPPED IN ADDITION WHERE THE ZONE TERMINATES; BY LENGTH EQUAL TO THE DEVELOPMENT LENGTH OF HIGHER DIA BAR.

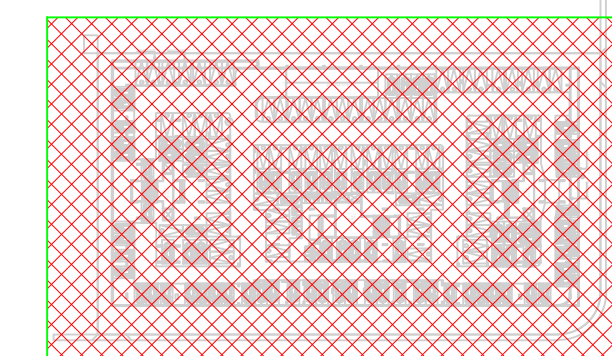

GRADE OF CONCRETE	
ALL STRUCTURAL ELEMENTS	M30

CONCRETE COVER	
FOOTINGS /RAFT	50MM
COLUMNS/SW	40MM
BEAMS	30MM
SLABS	25MM
PARDI WALLS	30MM

[illegible]

JOB TITLE / DEVELOPER

TURQUOISE-GRANDEUR
RATANA DEVELOPERS

DRAWING TITLE

STRUCTURAL LAYOUT AT FOUNDATION LEVEL

JOB NO 2111		DATE 16/04/2021		DRG. NO. S1-FDN-05		REVISION R0	
SCALE 1 : 100	SHEET SIZE A1/A2/A3		DRAWN BP		DESIGN KUNJ		CHECKED BHAVIK PATE

ARCHITECTS



HM ARCHITECTS
e:contact@hmarchitects.in

STRUCTURAL CONSULTANT

 **Blue
Skyz**
Engineers

email:blueskyzengineers@gmail.com