

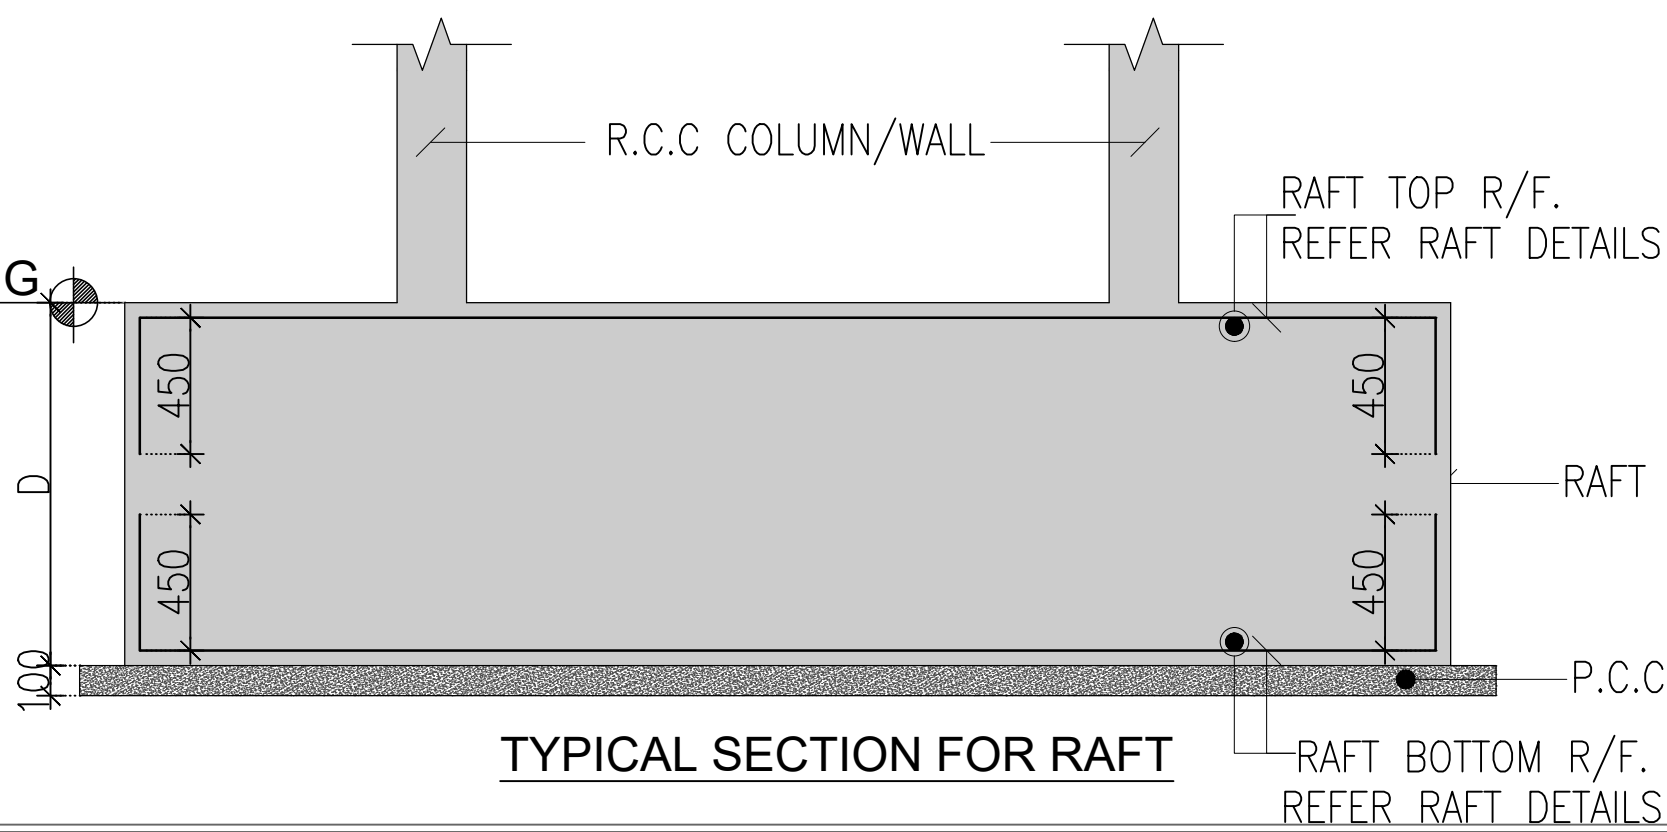
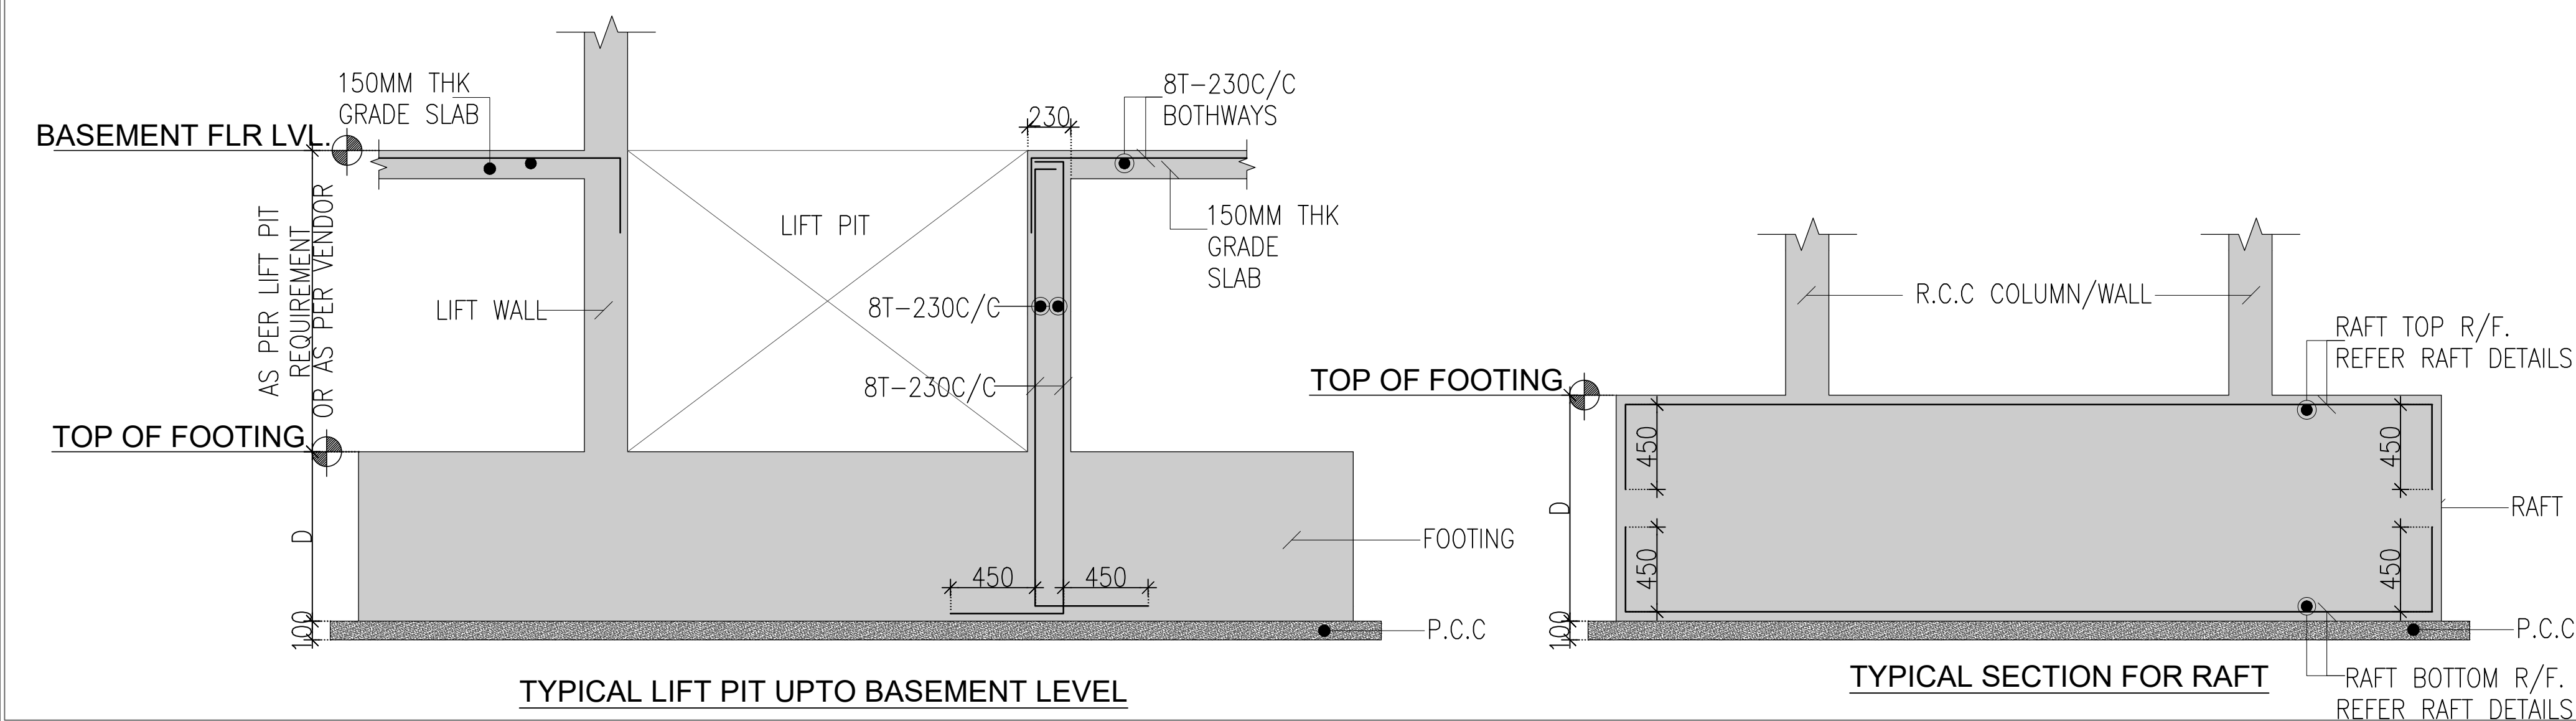
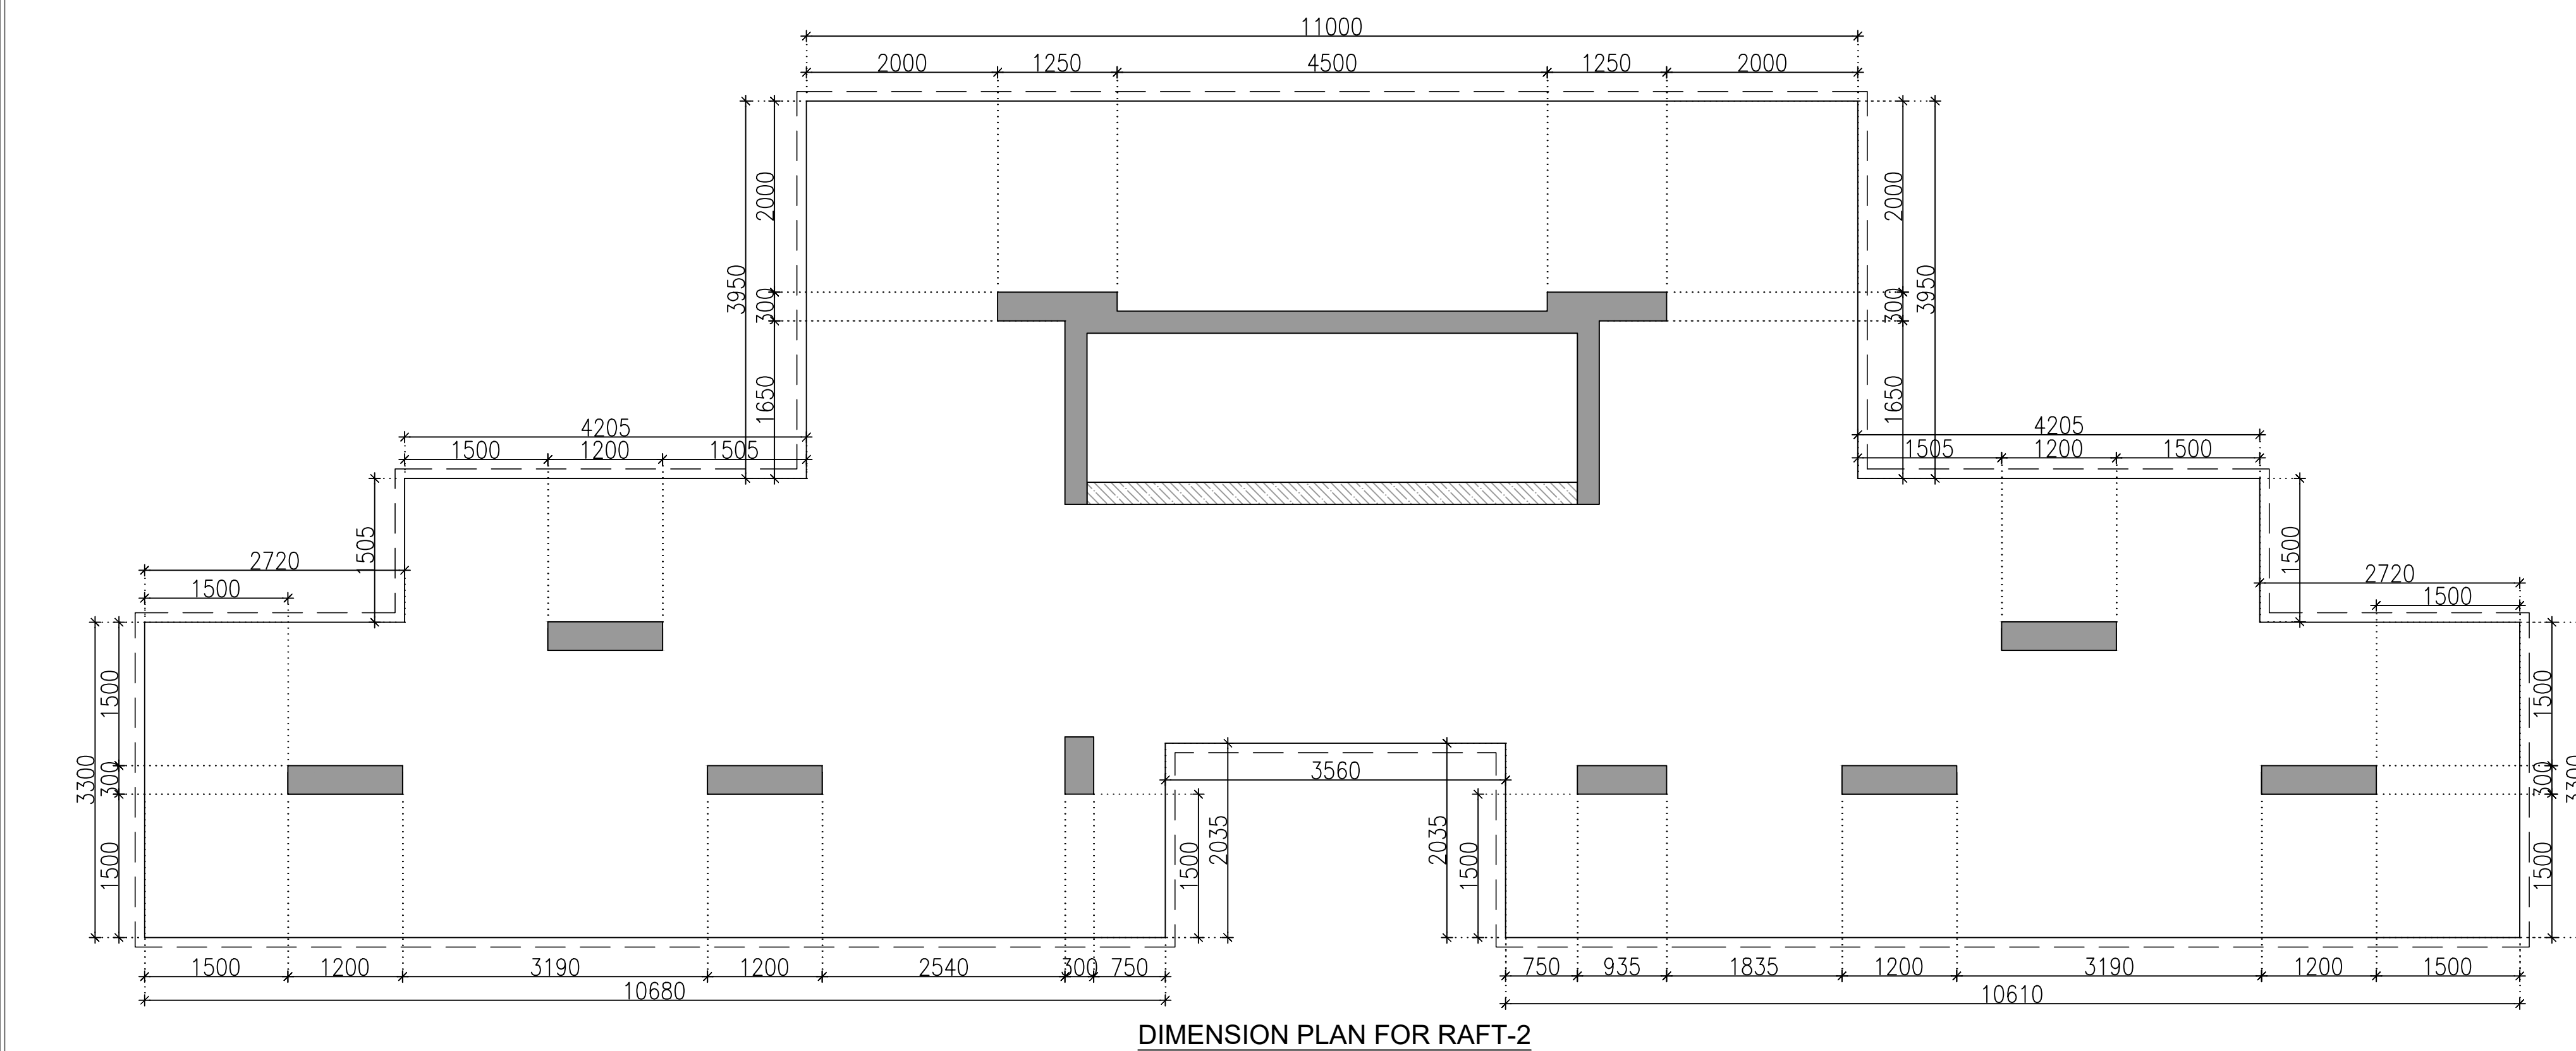
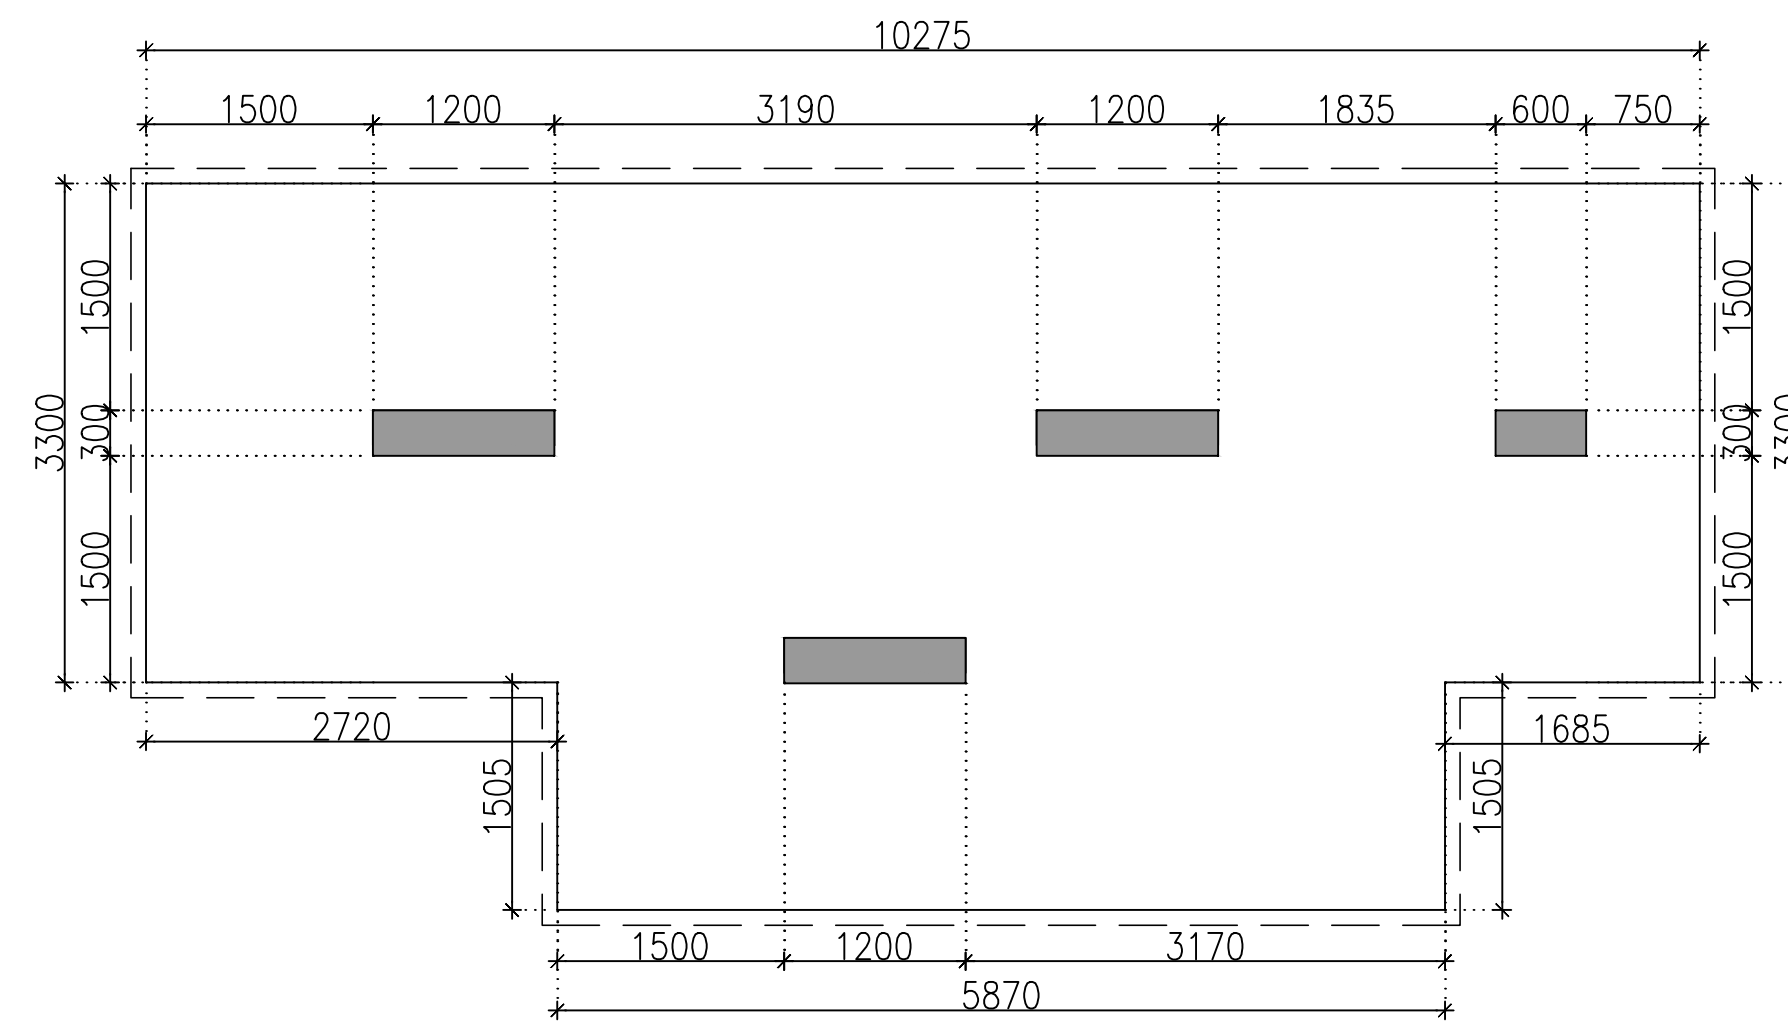


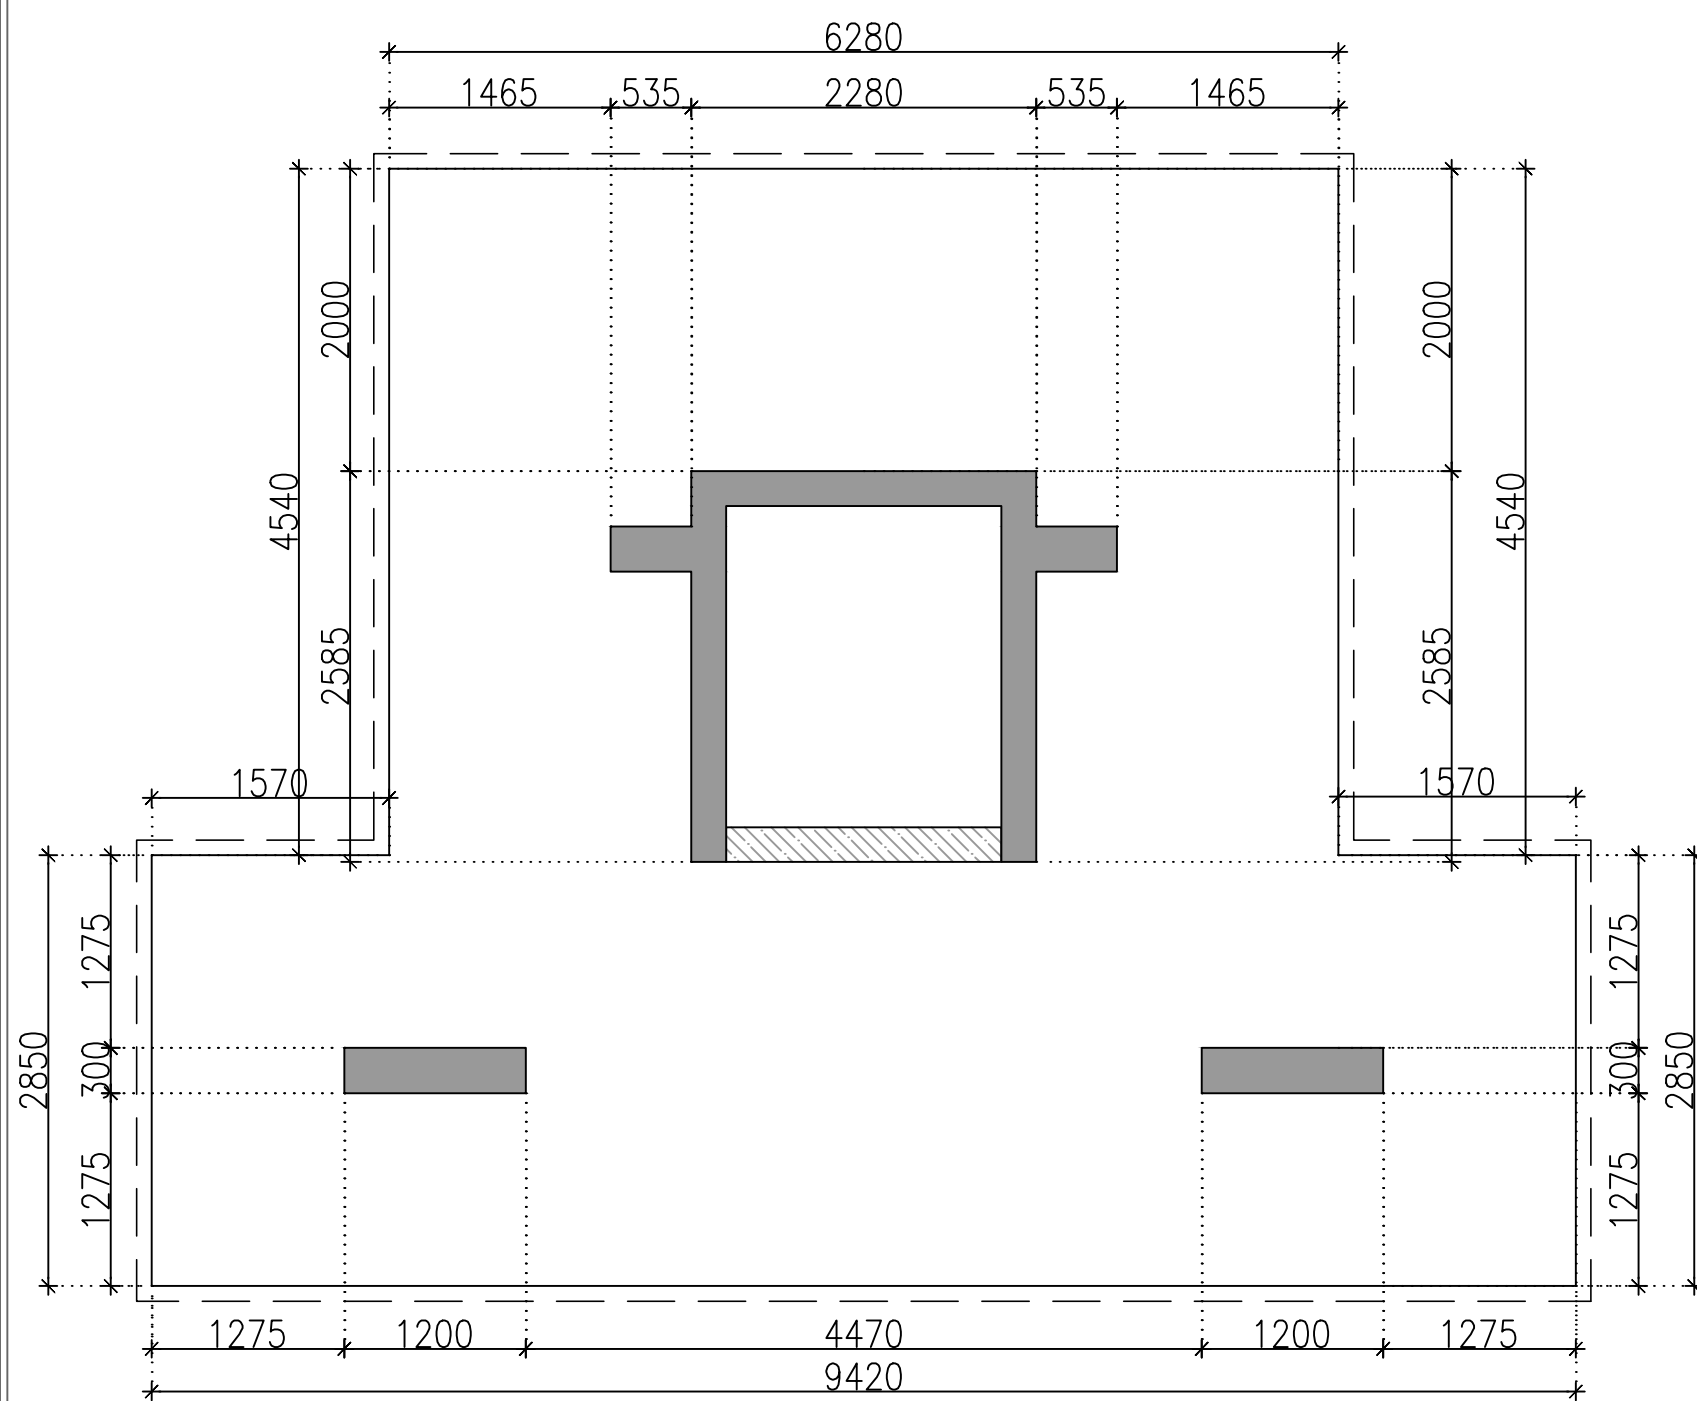

FOOTING SCHEDULE			
	RAFT-1	RAFT-2	RAFT-3
B' x L' (PCC)	REFER PLAN	REFER PLAN	REFER PLAN
B x L			
D	1000	1000	1000
T	—	—	—
STEEL // - B (SHORT SIDE) (BOTTOM FACE)	16T-100C/C	16T-100C/C	16T-100C/C
STEEL // - L (LONG SIDE) (BOTTOM FACE)	16T-100C/C	16T-100C/C	16T-100C/C
STEEL // - B (SHORT SIDE) (TOP FACE)	16T-100C/C	16T-100C/C	16T-100C/C
STEEL // - L (LONG SIDE) (TOP FACE)	16T-100C/C	16T-100C/C	16T-100C/C
REMARK	PAD FOOTING	PAD FOOTING	PAD FOOTING

- ### GENERAL NOTES :-
1. ALL DIMENSIONS ARE IN MM.
 2. FOR ALL NOTES, REFER OUR DRG NO: SO-01 TO SO-09.
 3. CEMENT SHALL BE OPC 43 GRADE OR HIGHER / AS PER TENDER SPECIFICATIONS & PORTABLE WATER SHOULD BE USED.
 4. SUPERVISION SHALL NOT BE OUR RESPONSIBILITY.
 5. TO TAKE OUT THE CUBE AND MATERIAL TESTING SHALL BE CONTRACTOR/ BUILDER/CLIENTS RESPONSIBILITY.
 6. LOAD TESTING OF STRUCTURE SHALL NOT BE OUR RESPONSIBILITY.
 7. ALL DIMENSIONS ARE TO BE READ AND NOT TO BE MEASURED
 8. T OR # INDICATE STEEL FE 5000 GRADE TMT BARS.
 9. ALL CONC.MIX. M:30 UNLESS OTHERWISE SPECIFIED.
 - 10.LD = DEVELOPMENT LENGTH : $50 \times \phi$; WHERE, ϕ = DIA. OF BAR.
 - 11.ALL BRICK WORK SHALL BE IN C.M. (1:6)
 - 12.STRUCTURAL LAY OUT SHOULD BE REFER ONLY FOR STRUCTURAL DETAILING.
 - 13.PLEASE REFER ARCHITECTURAL DWG FOR LVLS. & SETTINGS OUT CENTERLINE DIMENSIONS. THE CENTERLINE PUT IN THIS STRUCTURAL FOUNDATION LAYOUT IS SIMPLY INDICATIVE OF LOCATION AND AS APPROVED BY ARCHITECT.
 - 14.PLEASE REFER ARCH. DWG. FOR FINAL LAY OUT.
 - 15.CONTRACTOR SHOULD INFORM ARCHITECT/STRUCTURAL CONSULTANT IN CASE OF ANY CHANGE IN EXISTING CONDITION FOUND, IMMEDIATELY
 - 16.THIS DRG. SHOULD BE READ ALONG WITH ARCHITECTURAL DRGS.AND ANY CHANGES/DEVIATION FOUND SHOULD BE IMMEDIATELY BROUGHT TO NOTICE OF ARCHITECT & STR. ENGINEER
 - 17.THIS DWG.SHOULD BE READ ALONG WITH RELEVANT DETAILS
 - 18.MIX DESIGN SHOULD BE GOT APPROVED PRIOR TO EXECUTION OF WORK
 - 19.ALL THE WORK (TOP/BOTTOM) OF DIFFERENT ZONE SHALL BE LAPPED IN ADDITION WHERE THE ZONE TERMINATES; BY LENGTH EQUAL TO THE DEVELOPMENT LENGTH OF HIGHER DIA. BAR.


KEY PLAN

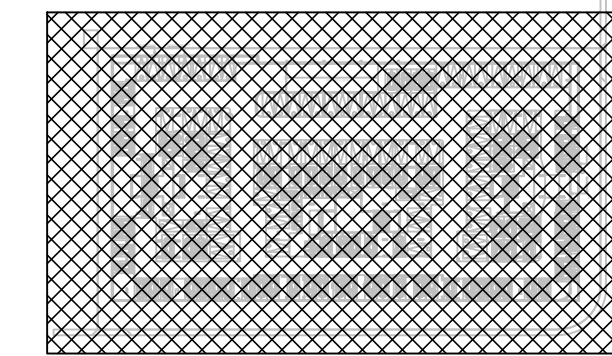

GRADE OF CONCRETE	
ALL STRUCTURAL ELEMENTS	M30

CONCRETE COVER	
FOOTINGS /RAFT	50MM
COLUMNS/SW	40MM
BEAMS	30MM
SLABS	25MM
PARDI WALLS	30MM

CONCRETE COVER	
FOOTINGS /RAFT	50MM
COLUMNS/SW	40MM
BEAMS	30MM
SLABS	25MM
PARDI WALLS	30MM

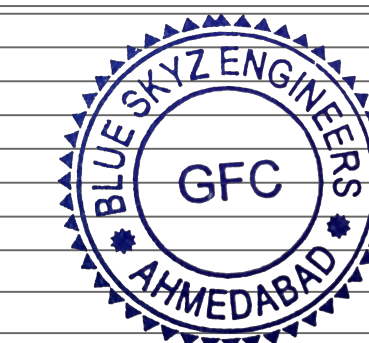

2	10-12-21	GOOD FOR CONSTRUCTION			
1	08-12-21	FOR REVIEW ONLY			
NO.	DATE	REVISION / REMARK	BY	DR	CH

JOB TITLE / DEVELOPER

TURQUOISE-GRANDEUR
RATANA DEVELOPERS

DRAWING TITLE


STRUCTURAL LAYOUT AT FOUNDATION LEVEL

JOB NO 2111		DATE 16/04/2021		DRG. NO. S1-FDN-05		REVISION R0	
SCALE 1: 100	SHEET SIZE A1/A2/A3	DRAWN BP		DESIGN KUNJ		CHECKED BHAVIK PATEL	

ARCHITECTS



STRUCTURAL CONSULTANT

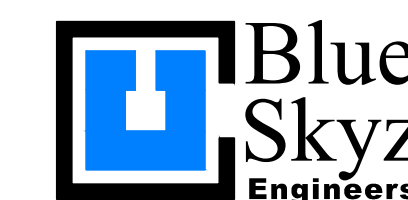

email:blueskyengineers@gmail.com